




03 ELEVACÃO 01
ESCALA 1/100

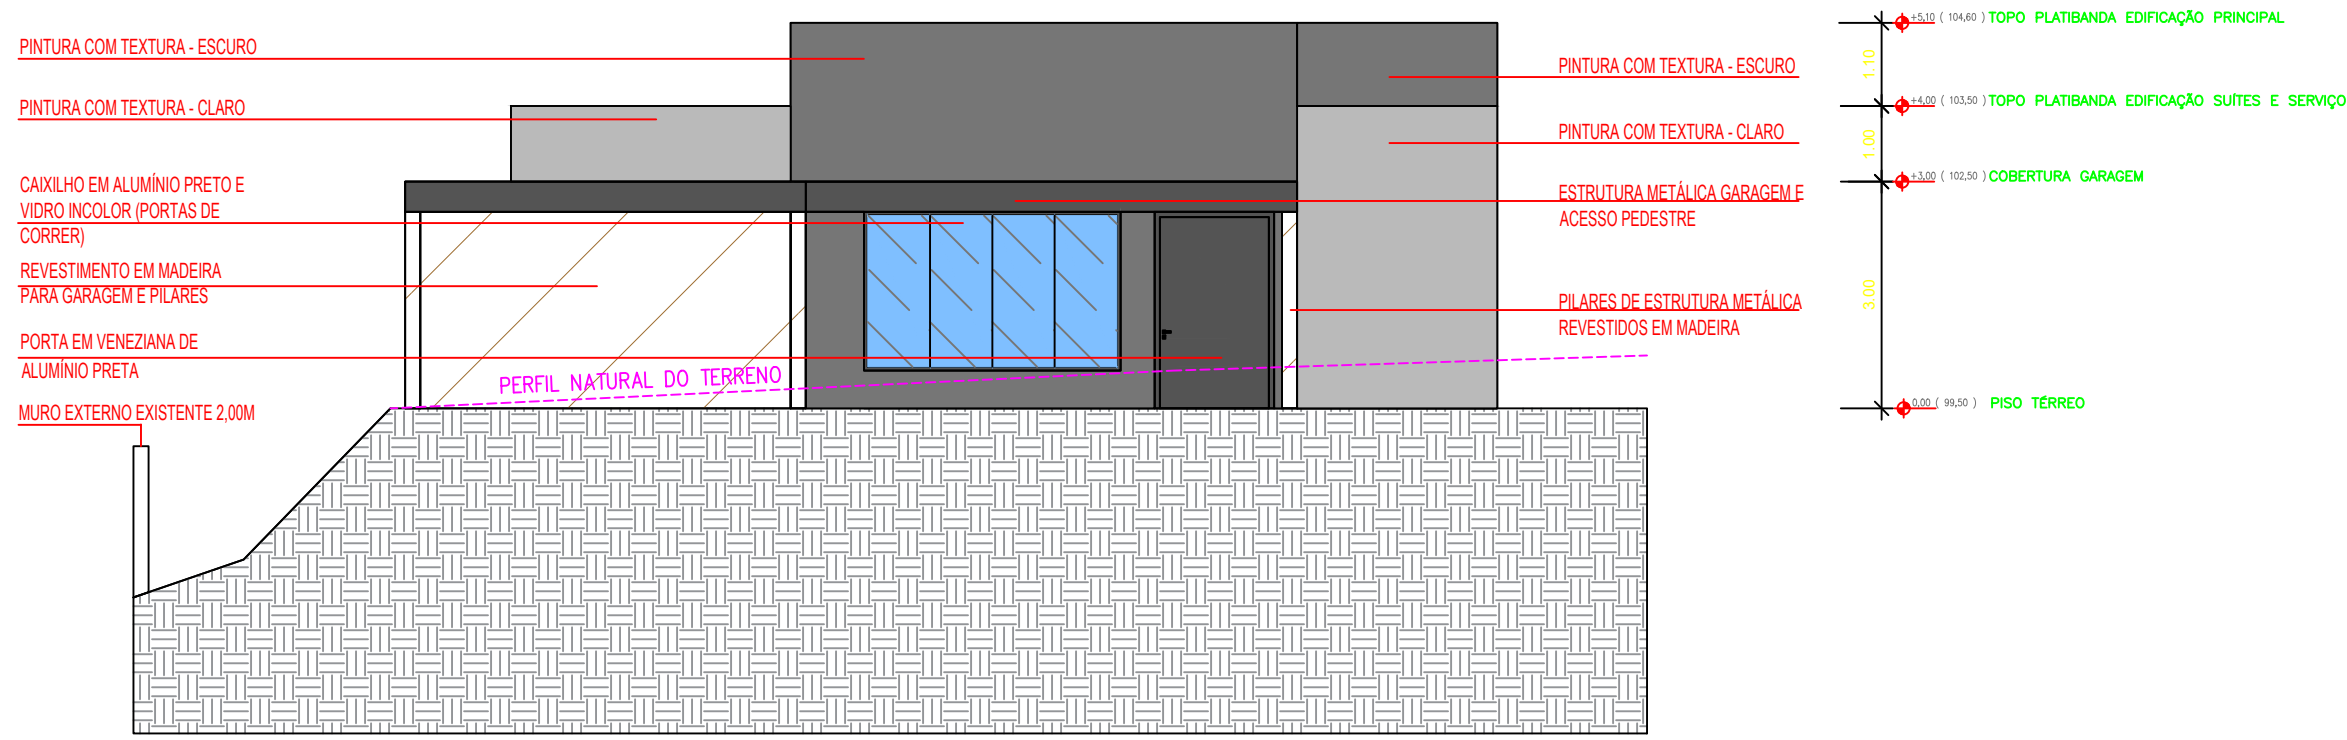


04 ELEVACÃO 02
ESCALA 1/100

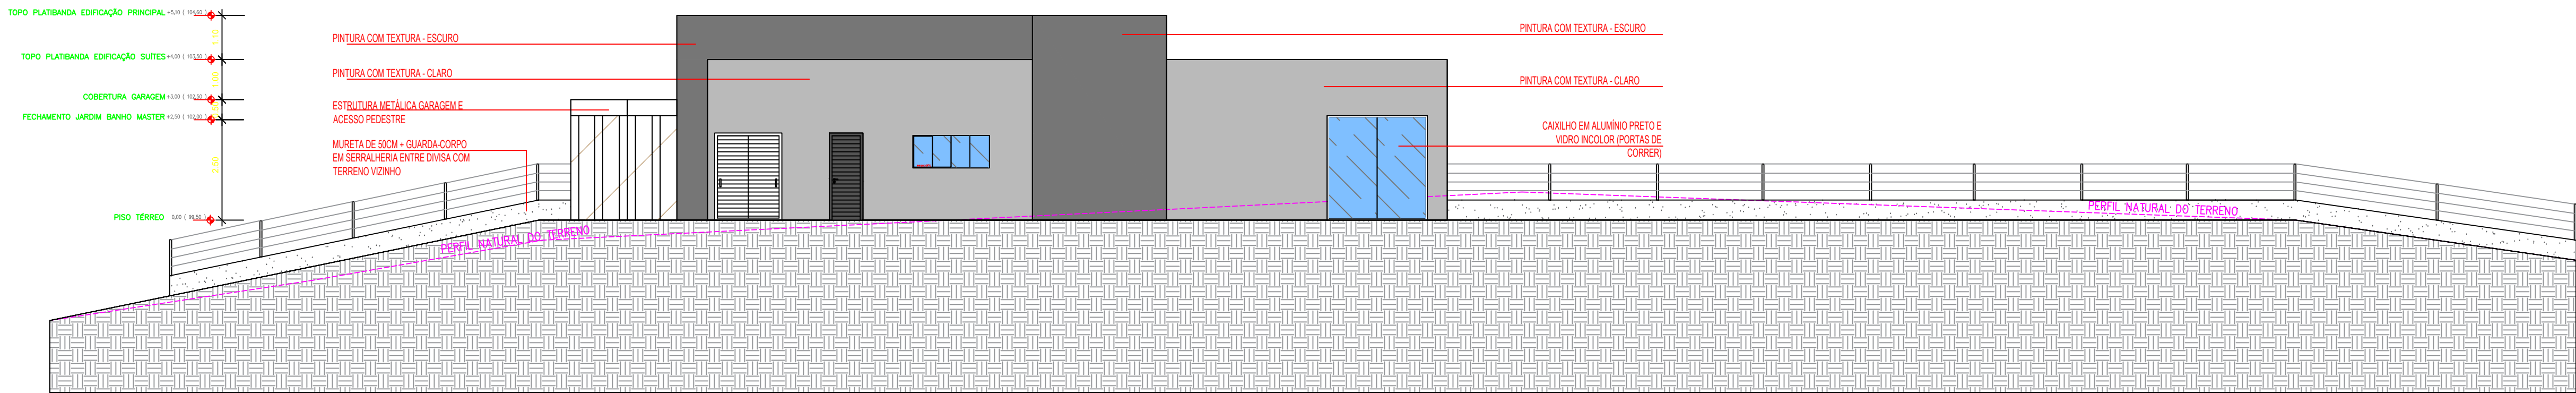

05 ELEVACÃO 03
ESCALA 1/100

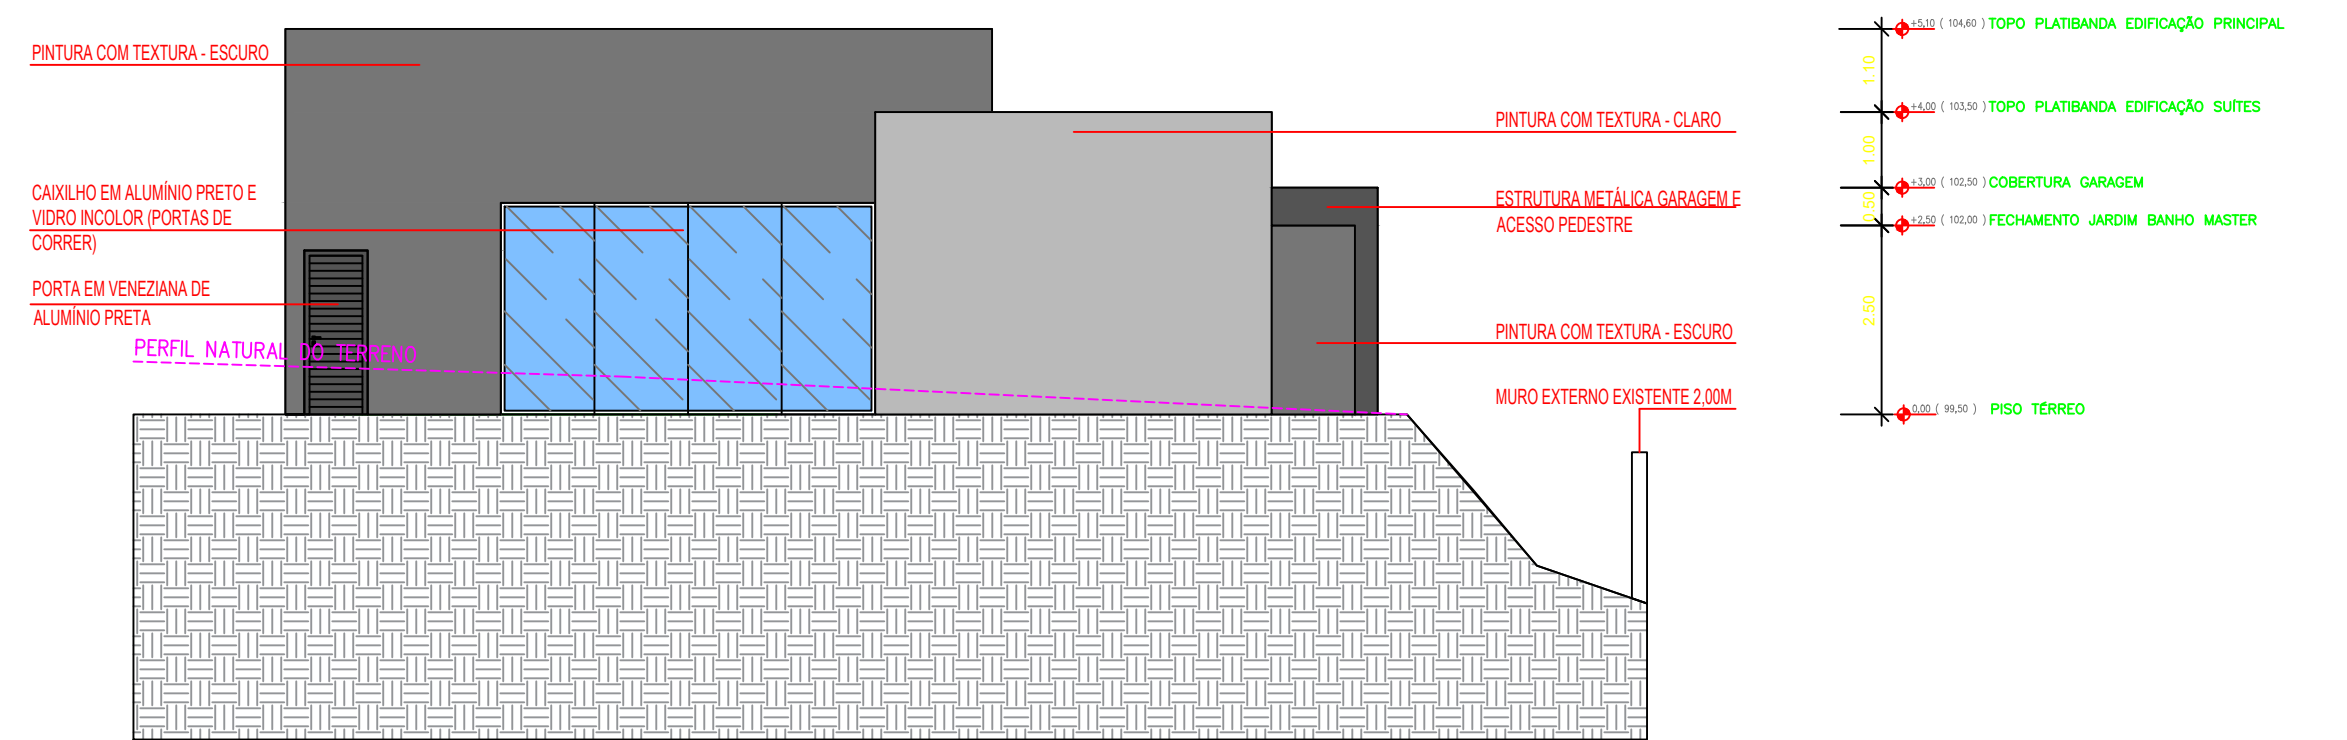


06 ELEVACÃO 04
ESCALA 1/100

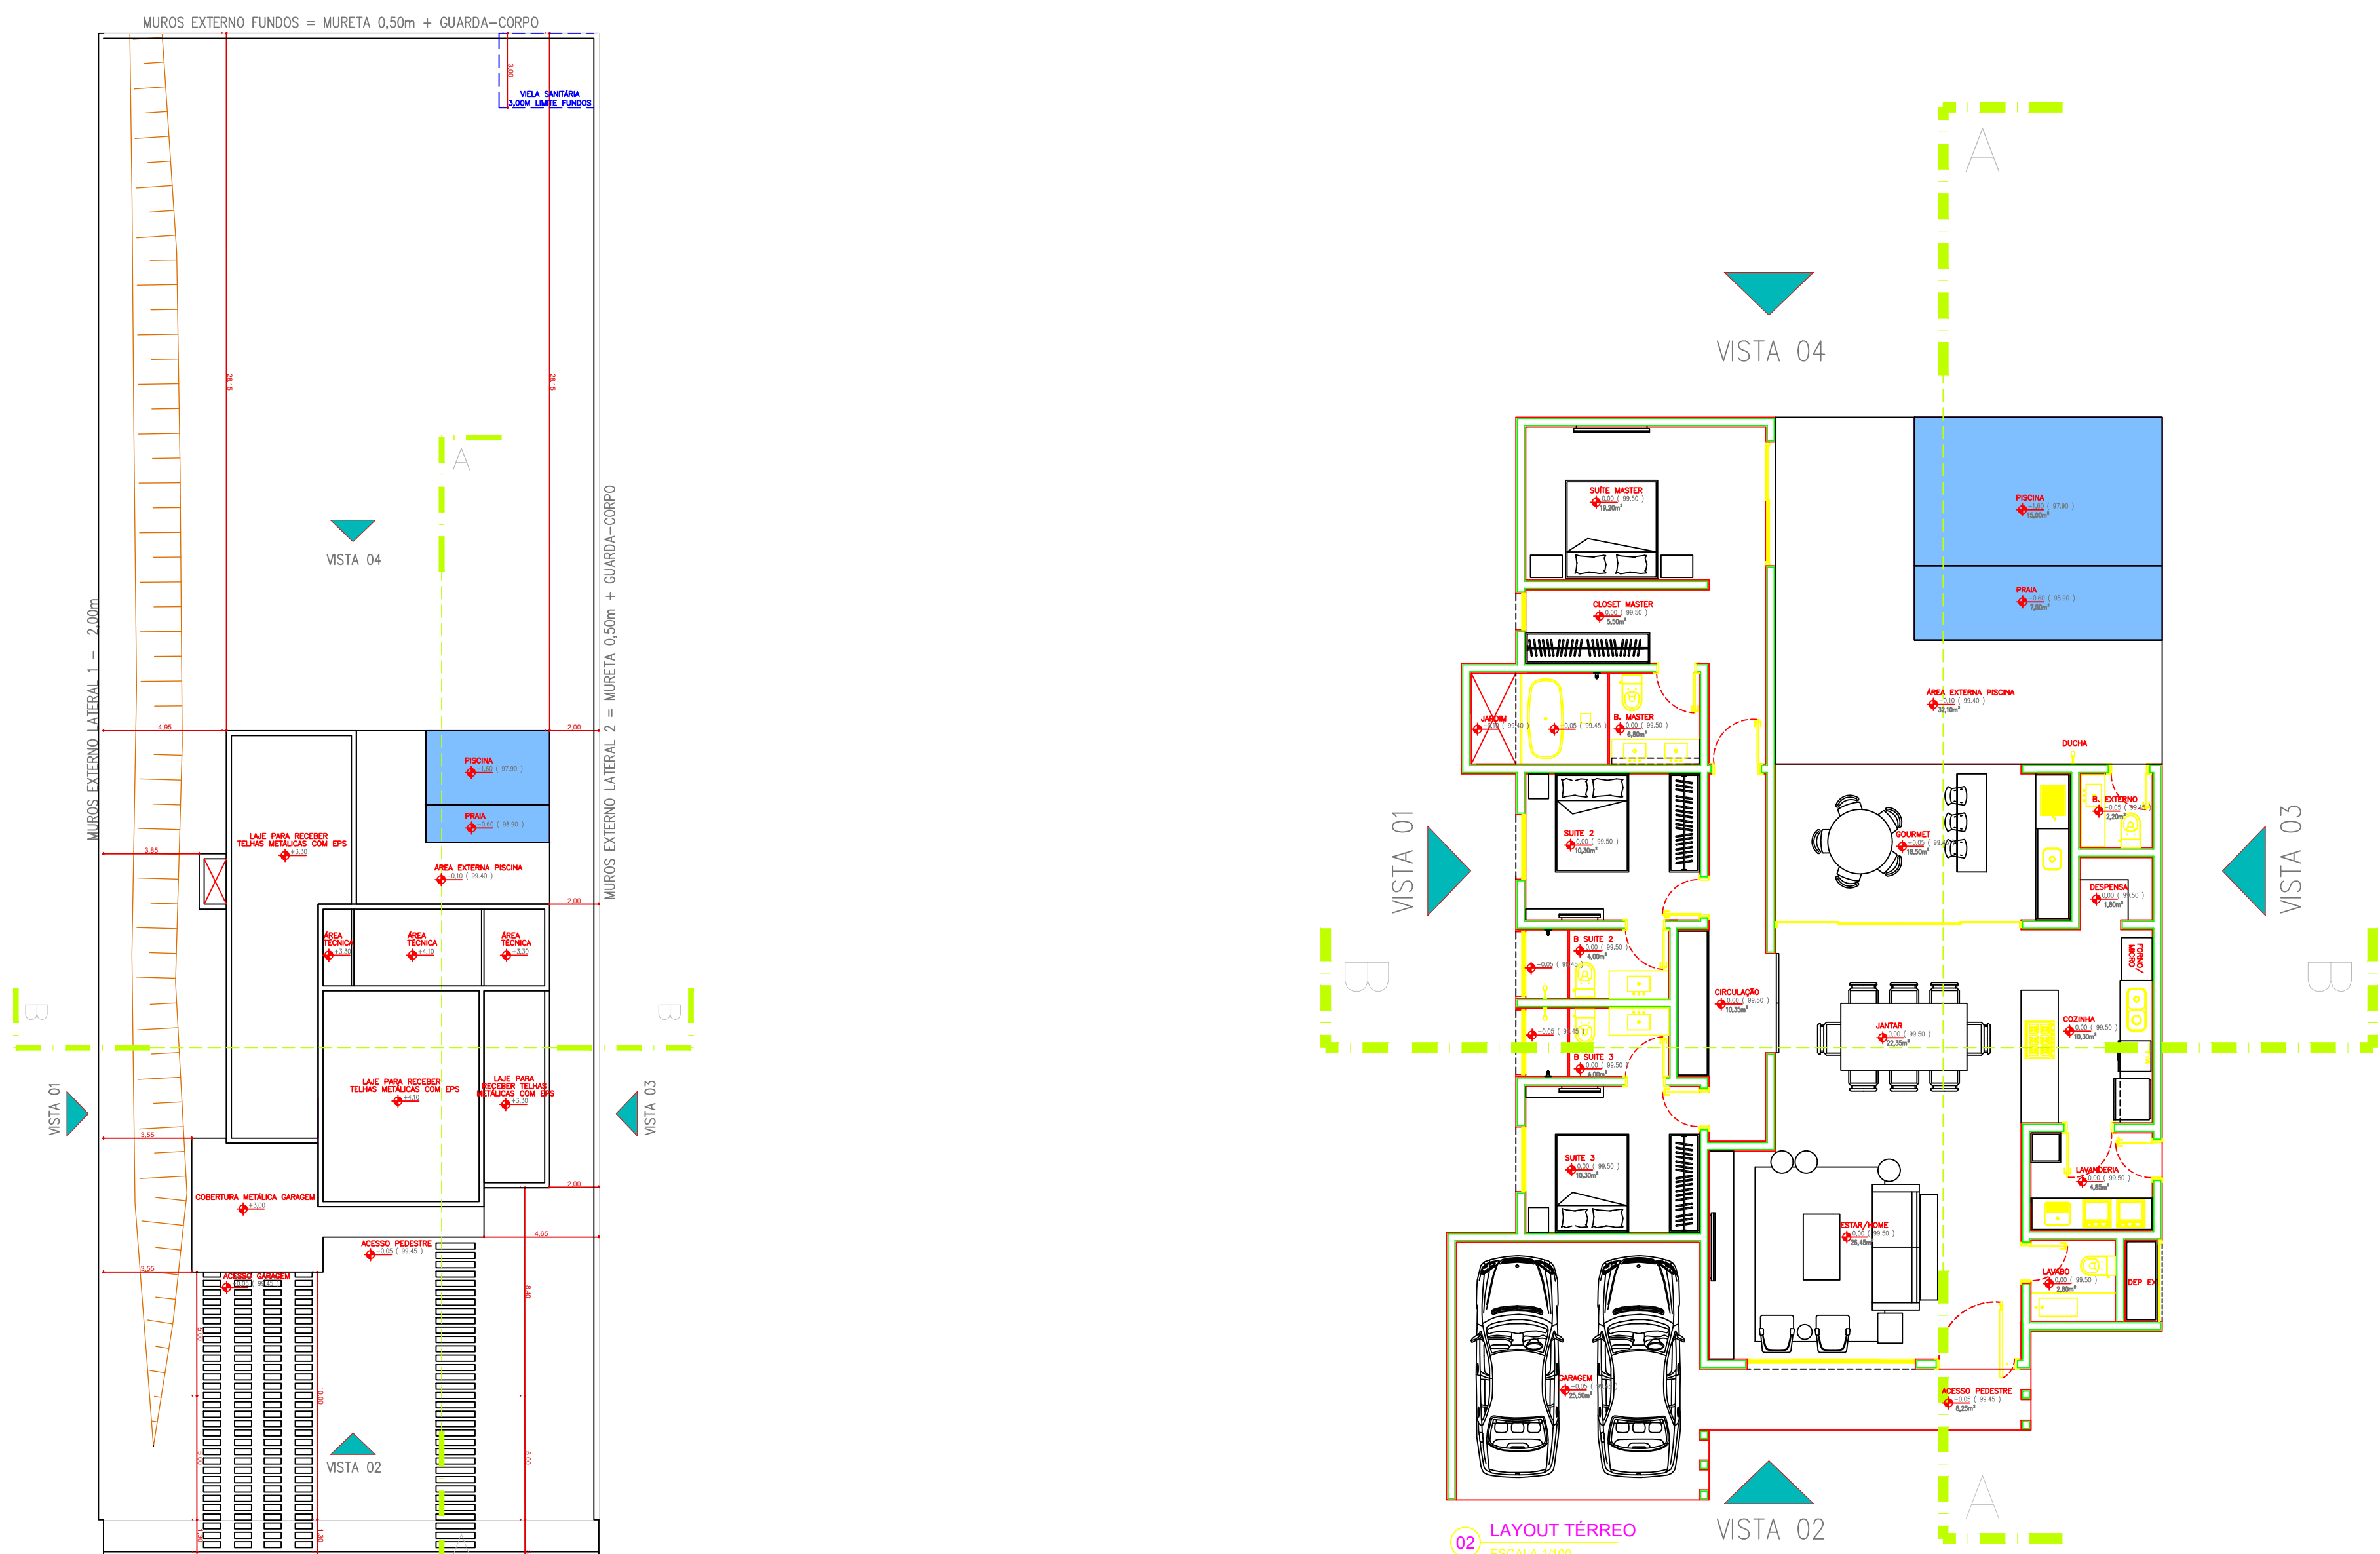


01 IMPLANTAÇÃO
ESCALA 1/200

02 LAYOUT TERREO
ESCALA 1/100

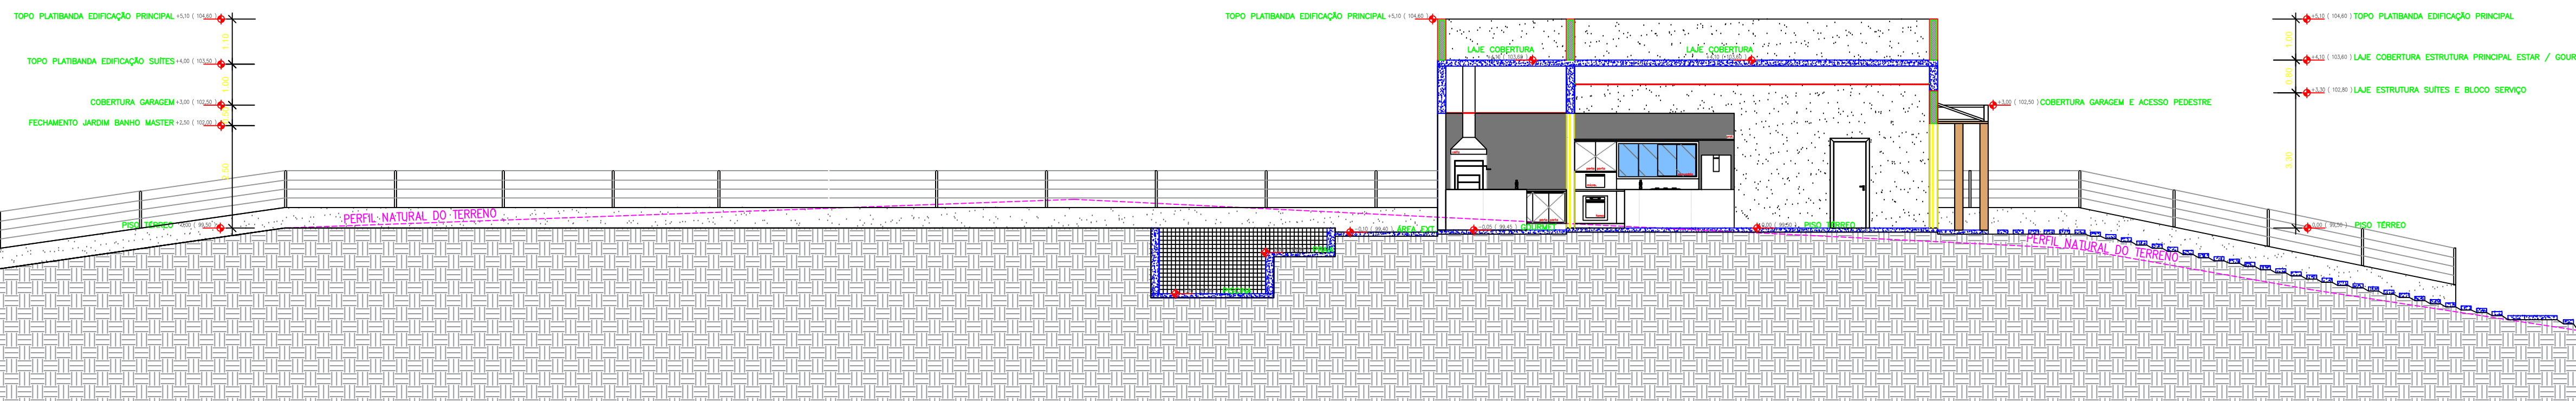

07 CORTE AA
ESCALA 1/100

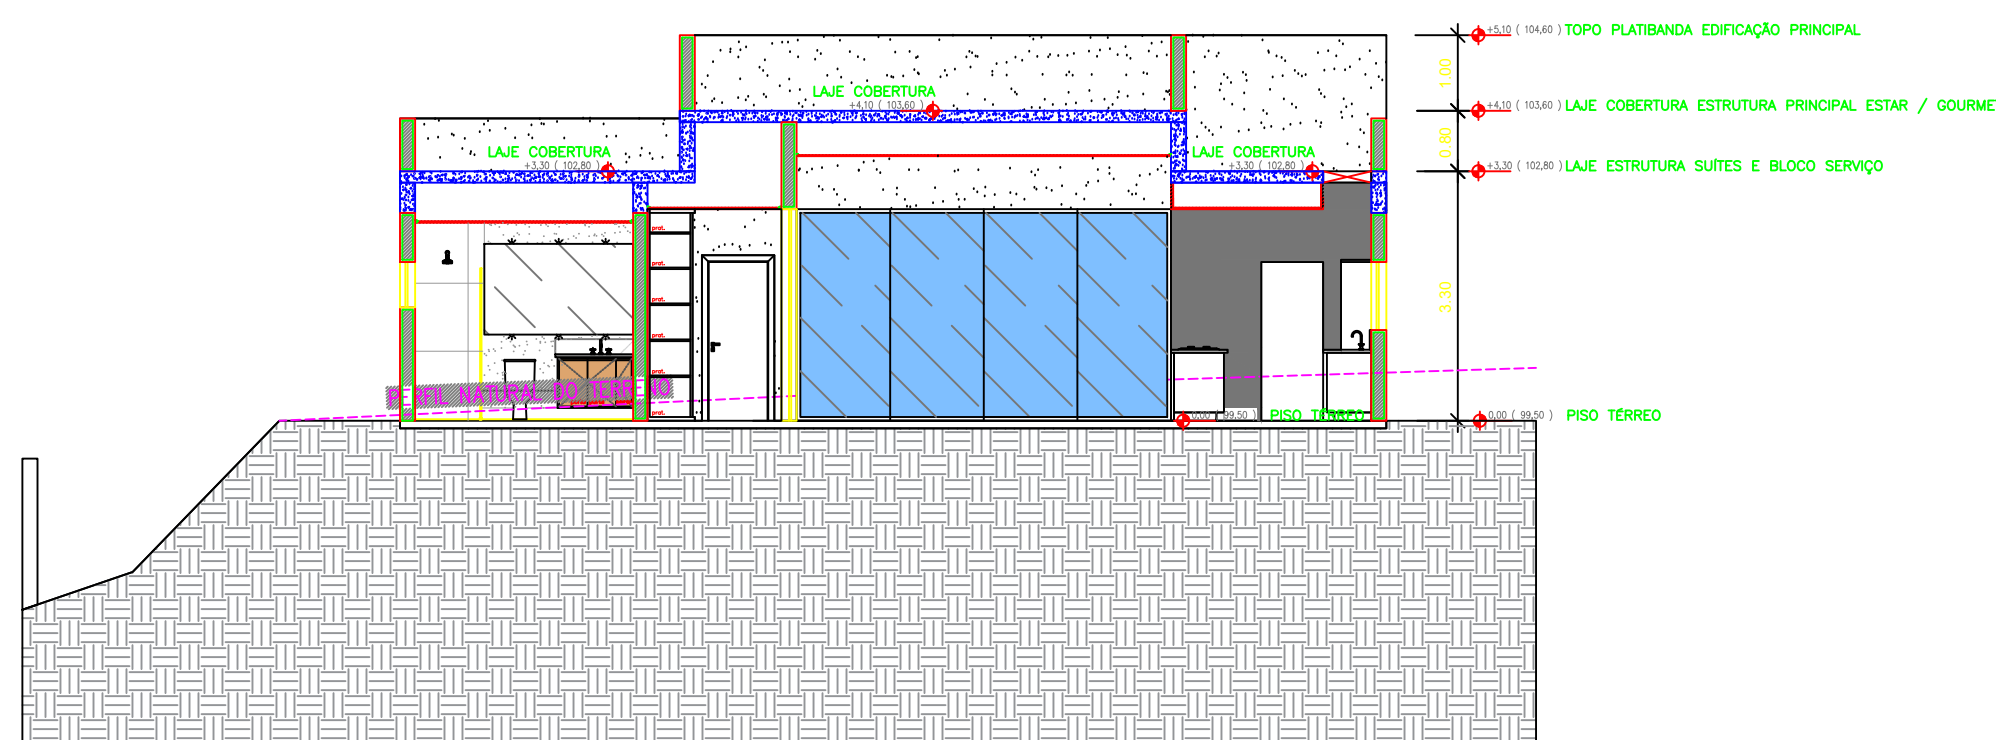


08 CORTE BB
ESCALA 1/100

PROJETO COMPLETO

FOLHA ÚNICA

ASSUNTO: CONSTRUÇÃO DE RESIDÊNCIA UNIFAMILIAR
LOCAL: ALAMEDA FREI SAMPAIO - LOTE 7 - QUADRA P
LOTEAMENTO JARDIM QUINTAS DA TERRACOTA - INDAIATUBA - SP
PROP.: MPH EMPREENDIMENTOS E INVESTIMENTOS IMOBILIÁRIOS LTDA
ESCALAS INDICADAS: ZONA ZRU - ROZA RURURBANA
Nº CAD: 5210.2250.0-8 CAT. USO: Ru

SITUAÇÃO SEM ESCALA

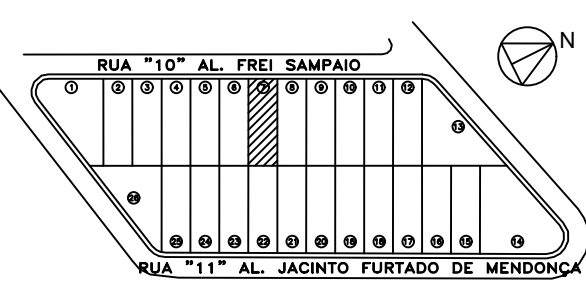

DECLARO QUE A APROVAÇÃO DO PROJETO NÃO IMPLICA NO RECONHECIMENTO POR PARTE DA PREFEITURA NO DIREITO DE PROPRIEDADE DO TERRENO.

MPH EMPREENDIMENTOS E INVESTIMENTOS IMOBILIÁRIOS LTDA
representante legal:
ARY CEZAR DIAS TRANQUILINI FILHO
CPF: 400.430.488-11

ÁREAS	(m²)
TERRENO	1.200,00
PAV. TERREO	219,60
PISCINA E PRAIA	22,50
TOTAL	242,10
LIVRE	957,90

Murilo Benatti
Eng: Civil CREA: 5.069.542.802
Responsável pela aprovação de projetos e fiscalização de obras em andamento junto à Associação dos proprietários e moradores do Loteamento Jardim Quintas da Terracota.